
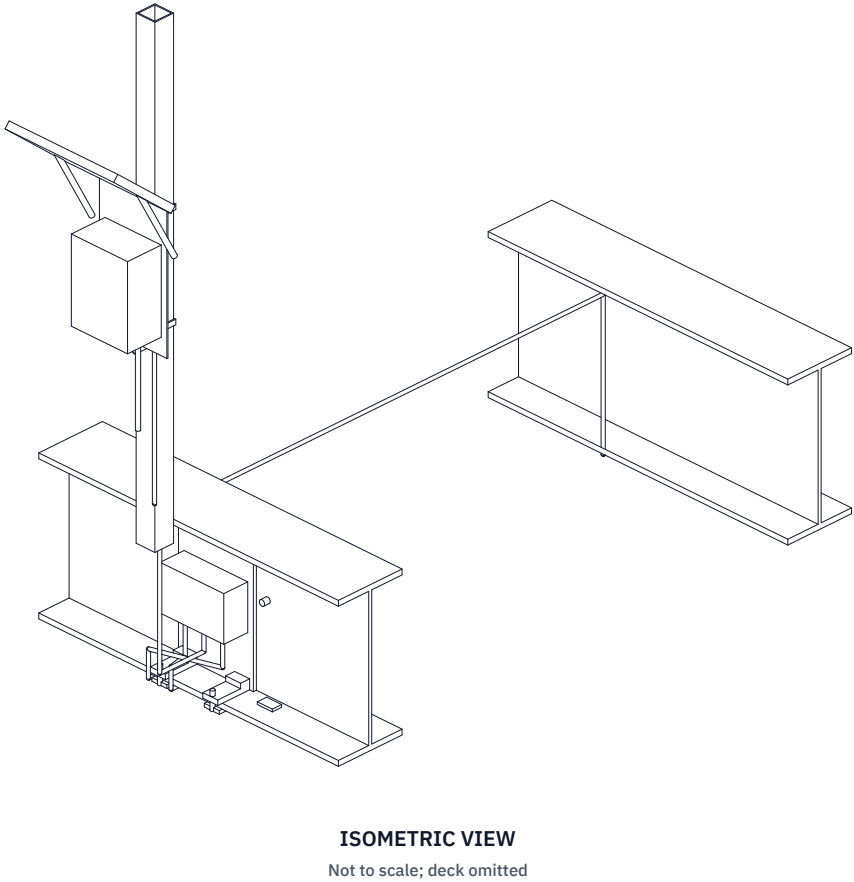
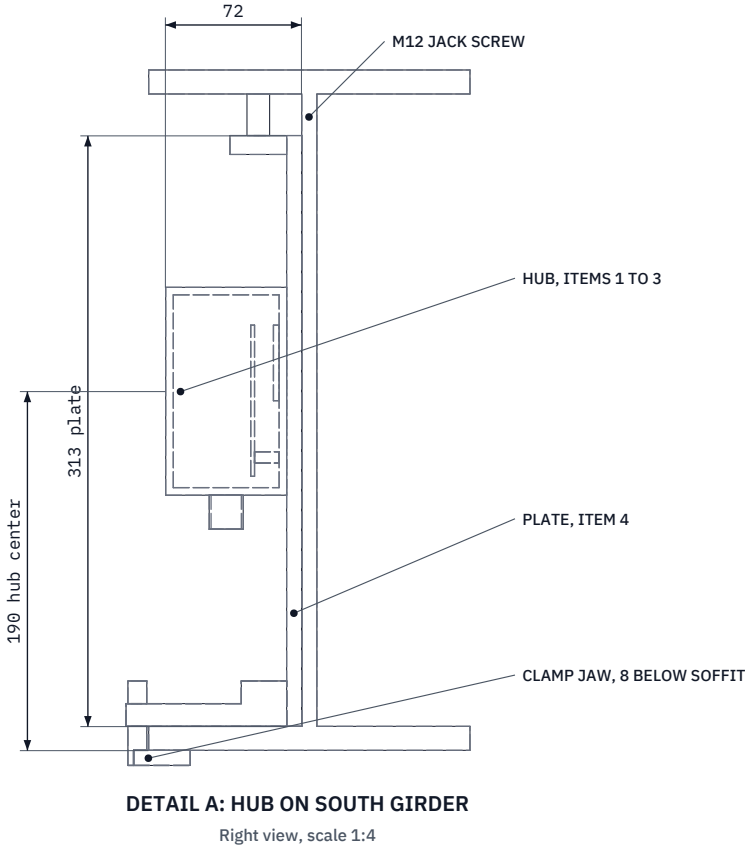


CONCEPT, NOT FOR FABRICATION
PRELIMINARY, NOT FOR FABRICATION

REV	DESCRIPTION	DATE	BY
P1	Preliminary GA for TRL 3 (from cad/src/model.py)	2026-09-25	AC

DECK AND HANDRAILS OMITTED FOR CLARITY; HUB AND FIELDNODE ON THE -Y (SOUTH) SIDE

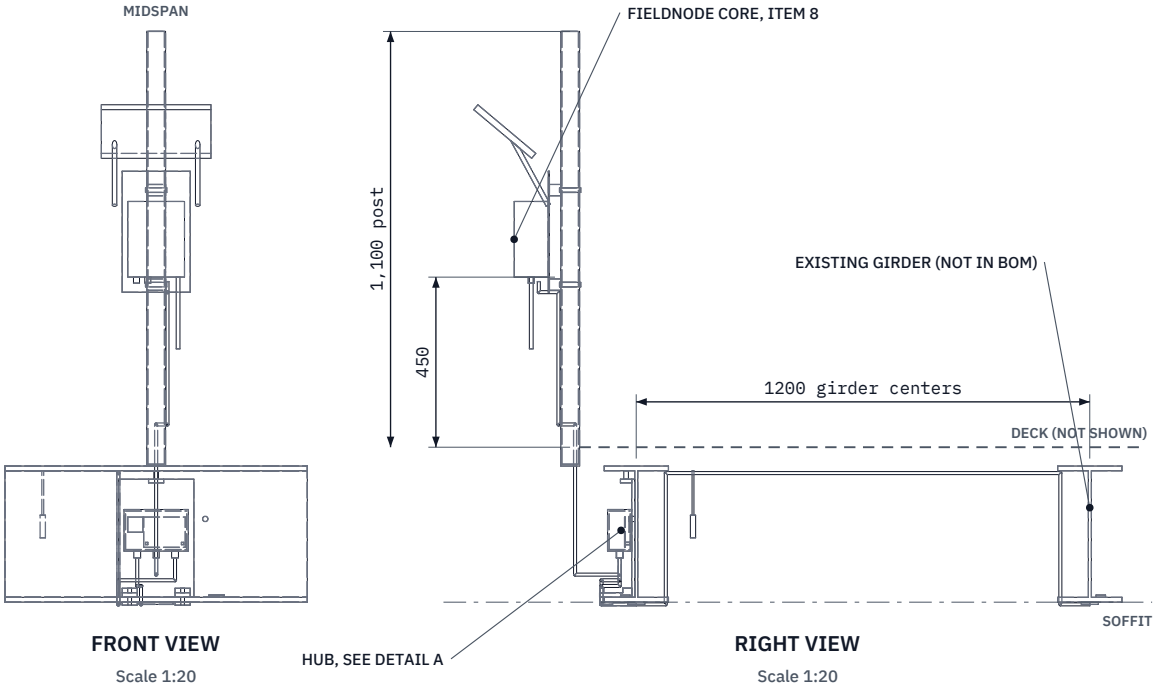

MAIN DIMENSIONS AND INTERFACES (MM)

Hub 170 x 64 x 110 IP67, 9 inside the flange tip line
Plate 200 x 313 x 8 Al on the bottom flange, jack to the top flange
Two flange-tip clamps at $x = \pm 70$; nothing drilled or welded
Gauge covers under each flange at midspan; 10 max below soffit (R9: 15)
FieldNode on the post, base 450 above deck; M12 5-pin, RS-485, 5 V
Example girders IPE 360 class at 1200 centers, span 6,400
Third-angle; front view from -Y; 800 segment at midspan ($x = 0$)

BRIDGEPULSE

General arrangement at midspan

DRAWING NO. BRP-DWG-001			REV P1	SHEET 1 of 1	SIZE ANSI B
SCALE 1:20	UNITS mm	PROJECTION 	DATE 2026-09-25		DRAWN Amish Chadha
MATERIAL / NOTES 6061 Al plate; bought-in parts per bom/bom.csv. PRELIMINARY, NOT FOR FABRICATION					
Licensed CERN-OHL-S-2.0 · Open Hardware Portfolio · amishchadha.com			Generated from cad/src; do not edit by hand		